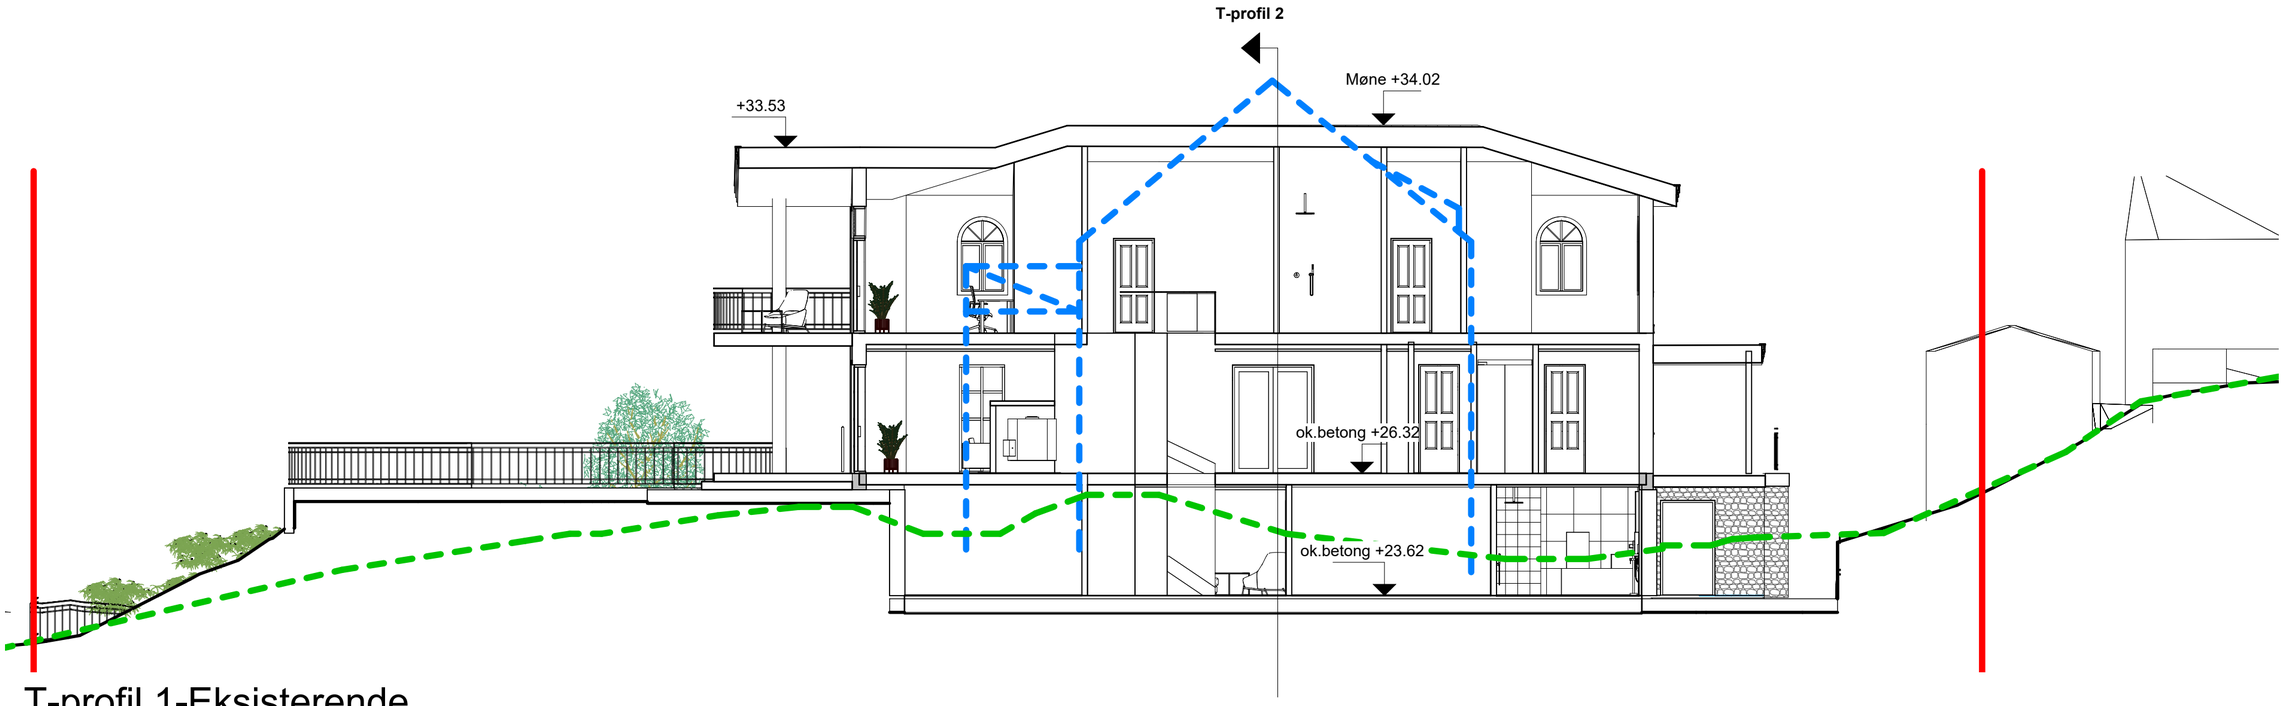

1 T-profil 1-Eksisterende

1 : 100

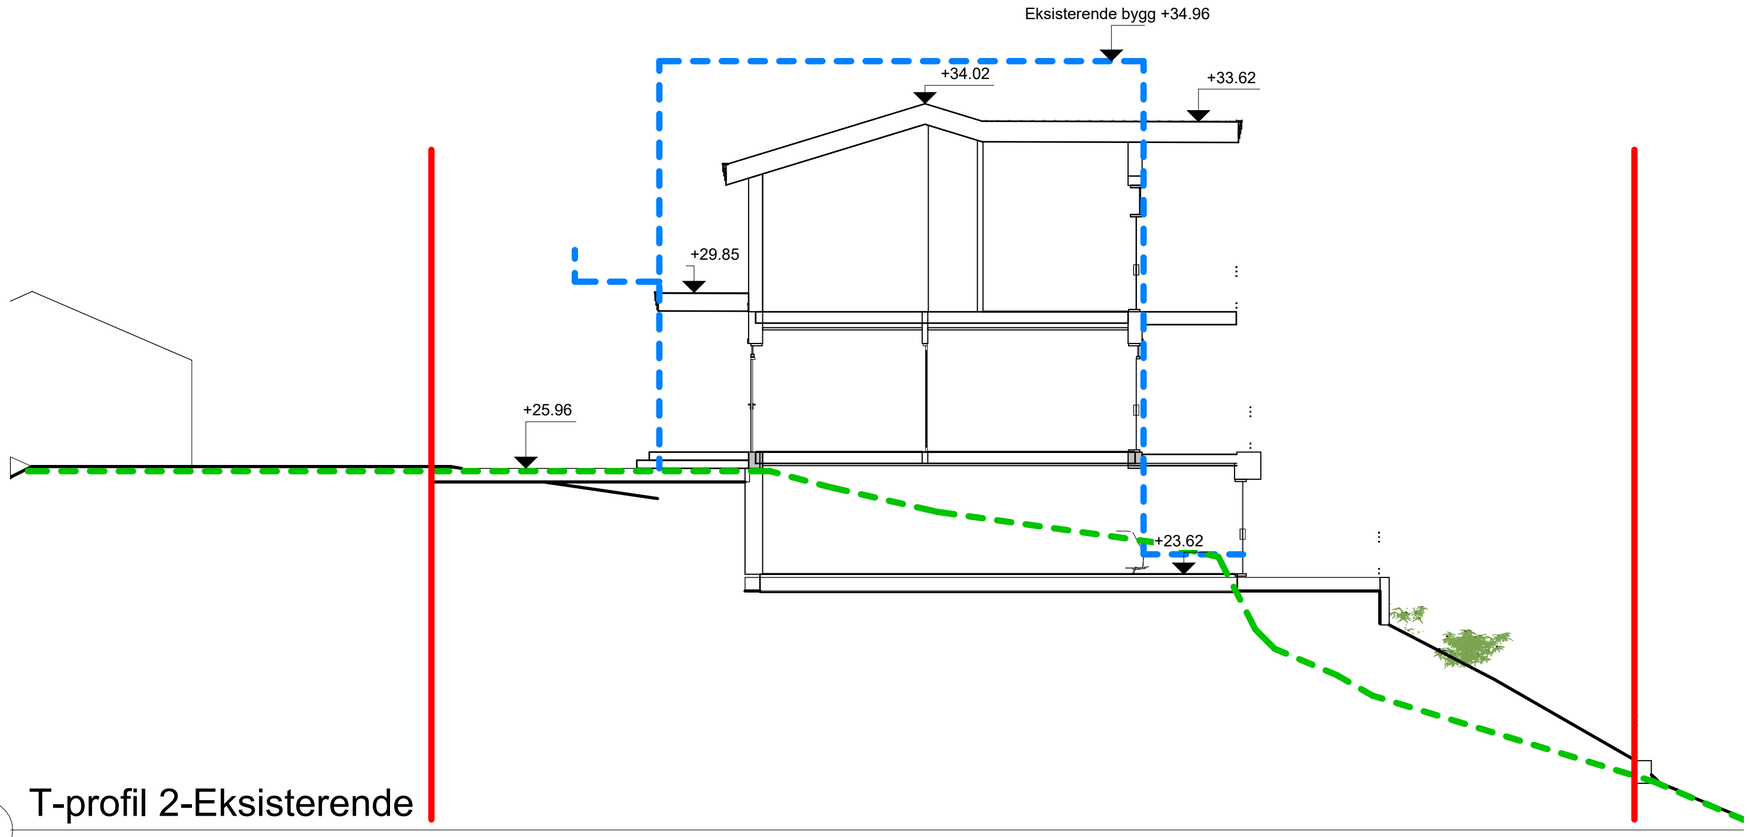

2 T-profil 2-Eksisterende

1 : 100

Eksisterende bygg

Eksisterende terreng

Teig

Rev.	Dato	Beskrivelse	Sign	Kontr

Fase:
BYGGESØKNAD

Lokalisering:
Bergen kommune
Nygårdsvikveien 38

Tittel:
Silje Faugstad

Nygårdsvikveien 38

Enebolig med garasje

Tegn.: SAN
Rev.
Dato: 26.11.25
Format: A2
Målestokk: 1 : 100
Kontroll prosjekt
Sign.: RE
Kontroll: RE

Prosjektnr.: 1258
Tegningsnr.: A-20 03
Type tegning: Terrengprofiler m/eksisterende bygg

ARKITEKT ROLV EIDE AS
Tel: 56332380
Postboks 325 5343 Straume
E-post: post@arkrolveide.no
www.arkrolveide.no