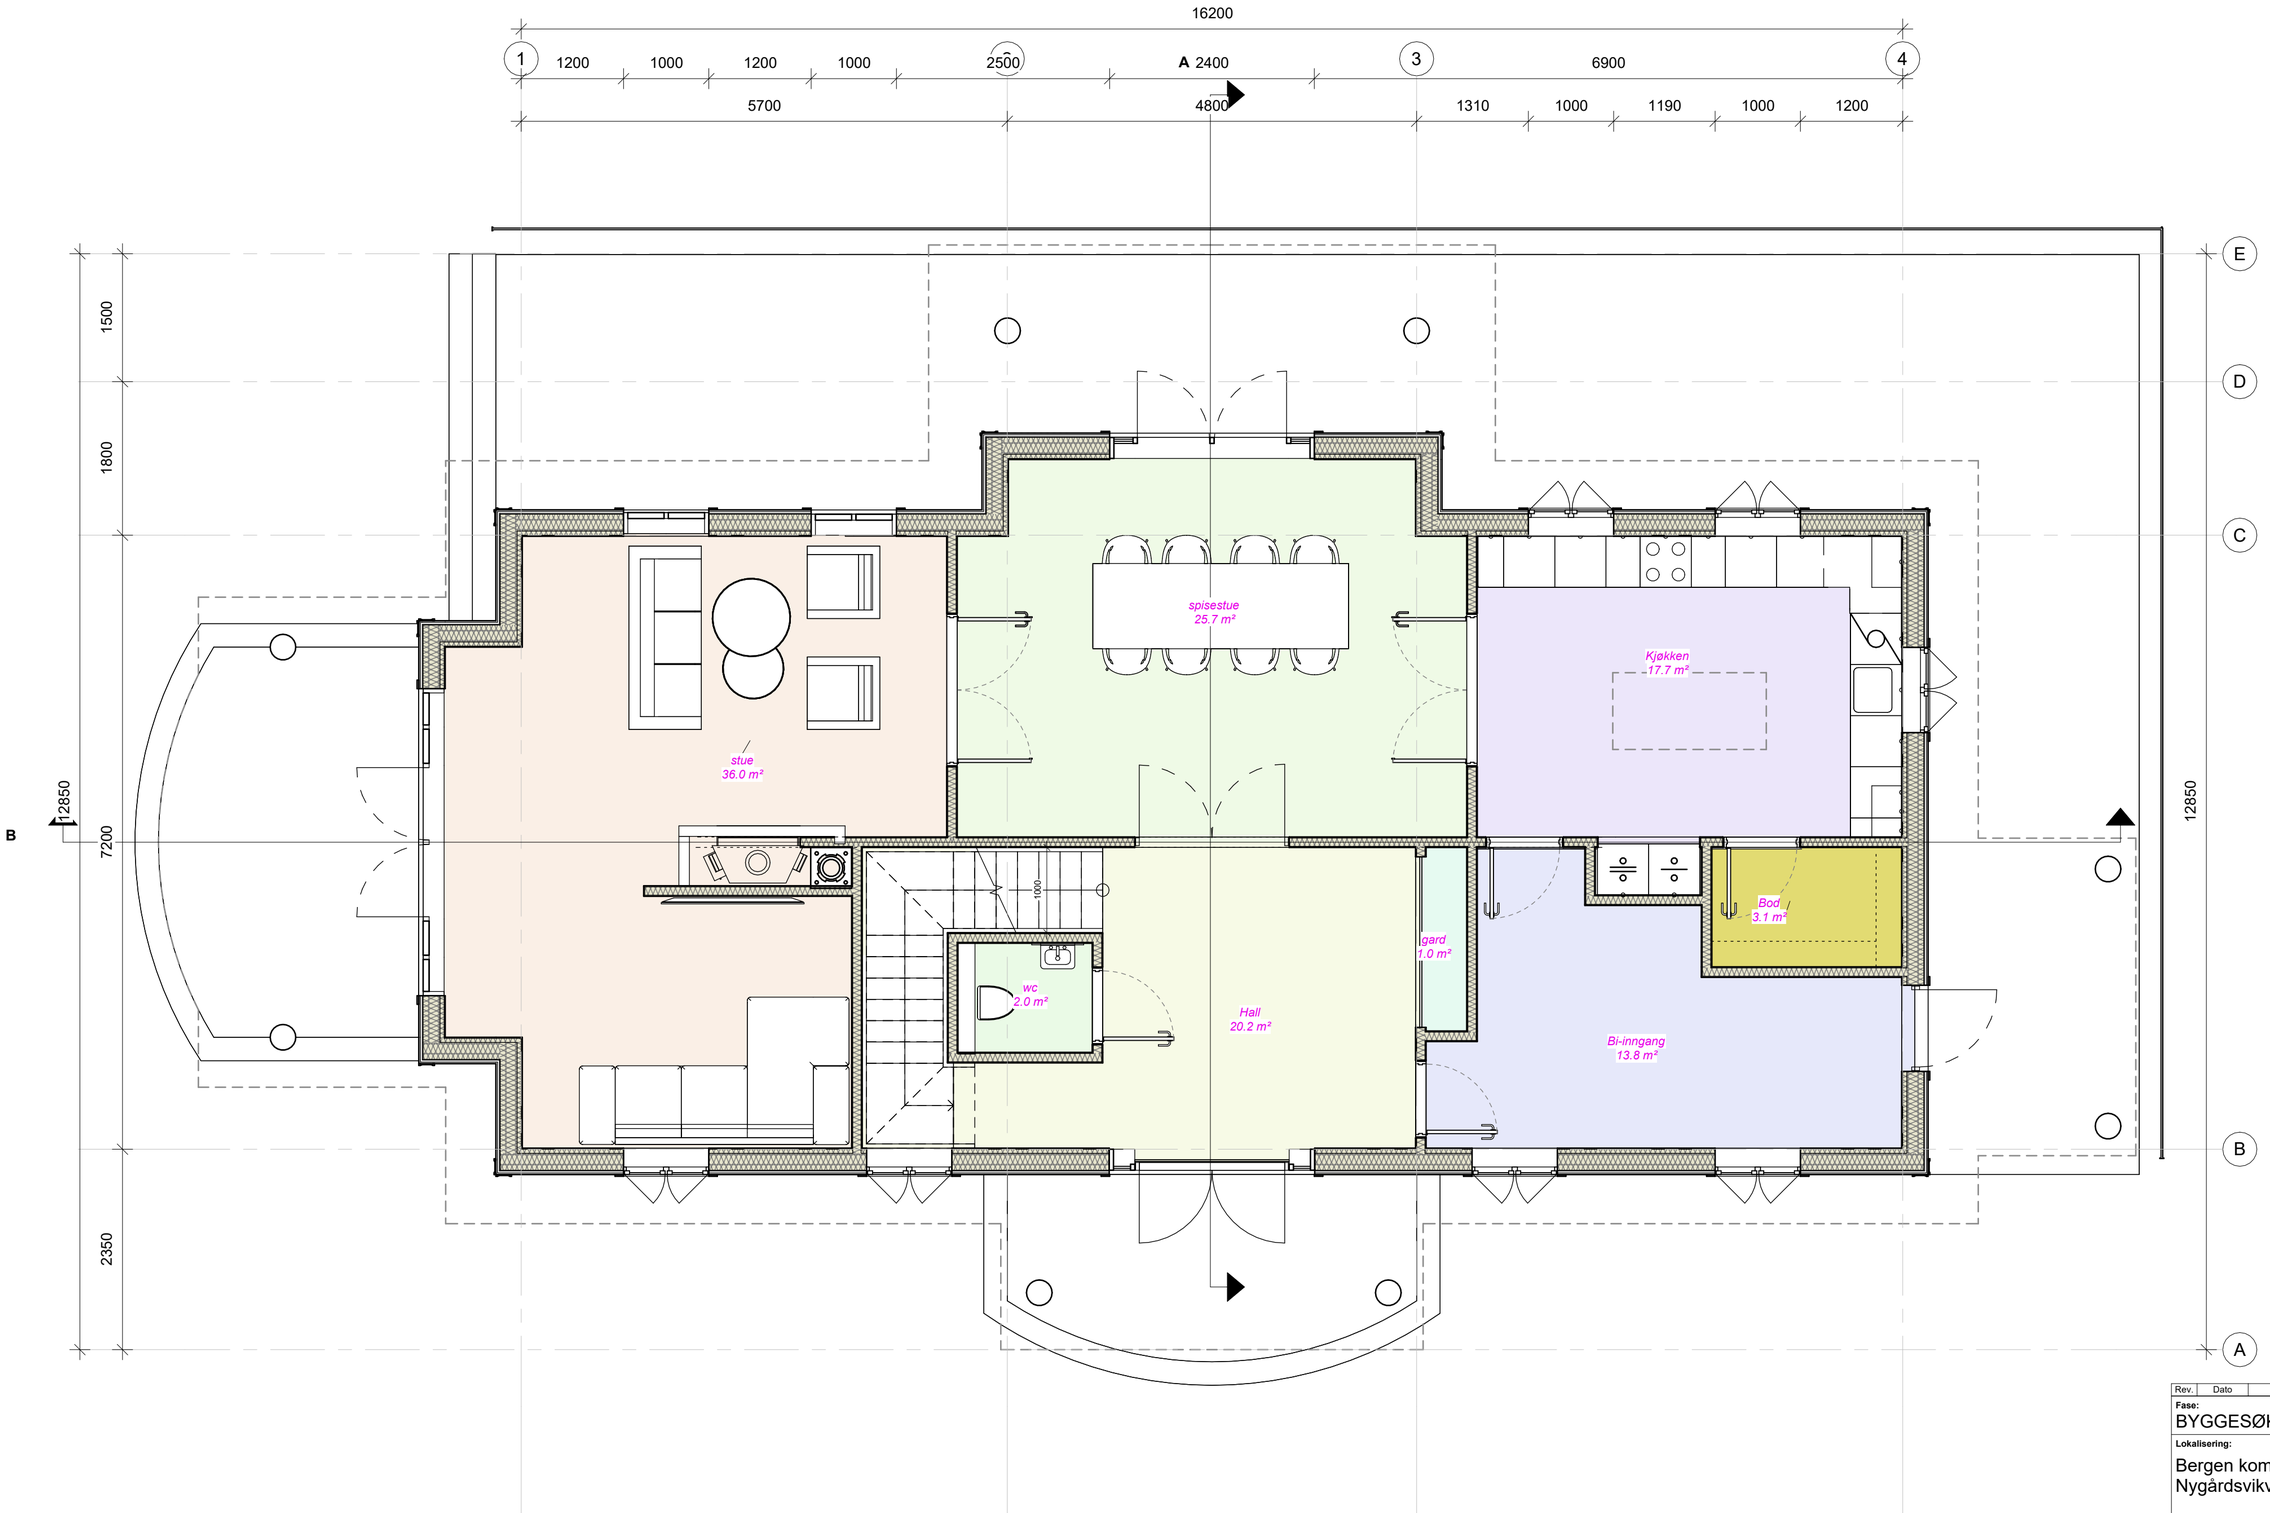


| Rev. | Dato | Beskrivelse | Sign | Kontr |
|---|---|---|---|---|

**Fase:**
BYGGESØKNAD

**Lokalisering:**
Bergen kommune
Nygårdsvikveien 38

**Tittel:**
Enebolig Silje Faugstad

Nygårdsvikveien 38

**Tegn.:** SAN
**Dato:** 26.11.25
**Rev.**
**Format:** A2
**Målestokk:** 1 : 50
**Kontroll prosjekt**
**Sign.:** RE
**Kontroll:** RE

**Prosjektnr.:** 1258
**Tegningsnr.:** A-30 02
**Type tegning:** Plan 02

ARKITEKT ROLV EIDE AS
Tel: 56332380
Postboks 325 5343 Straume
E-post: post@arkrolveide.no
www.arkrolveide.no