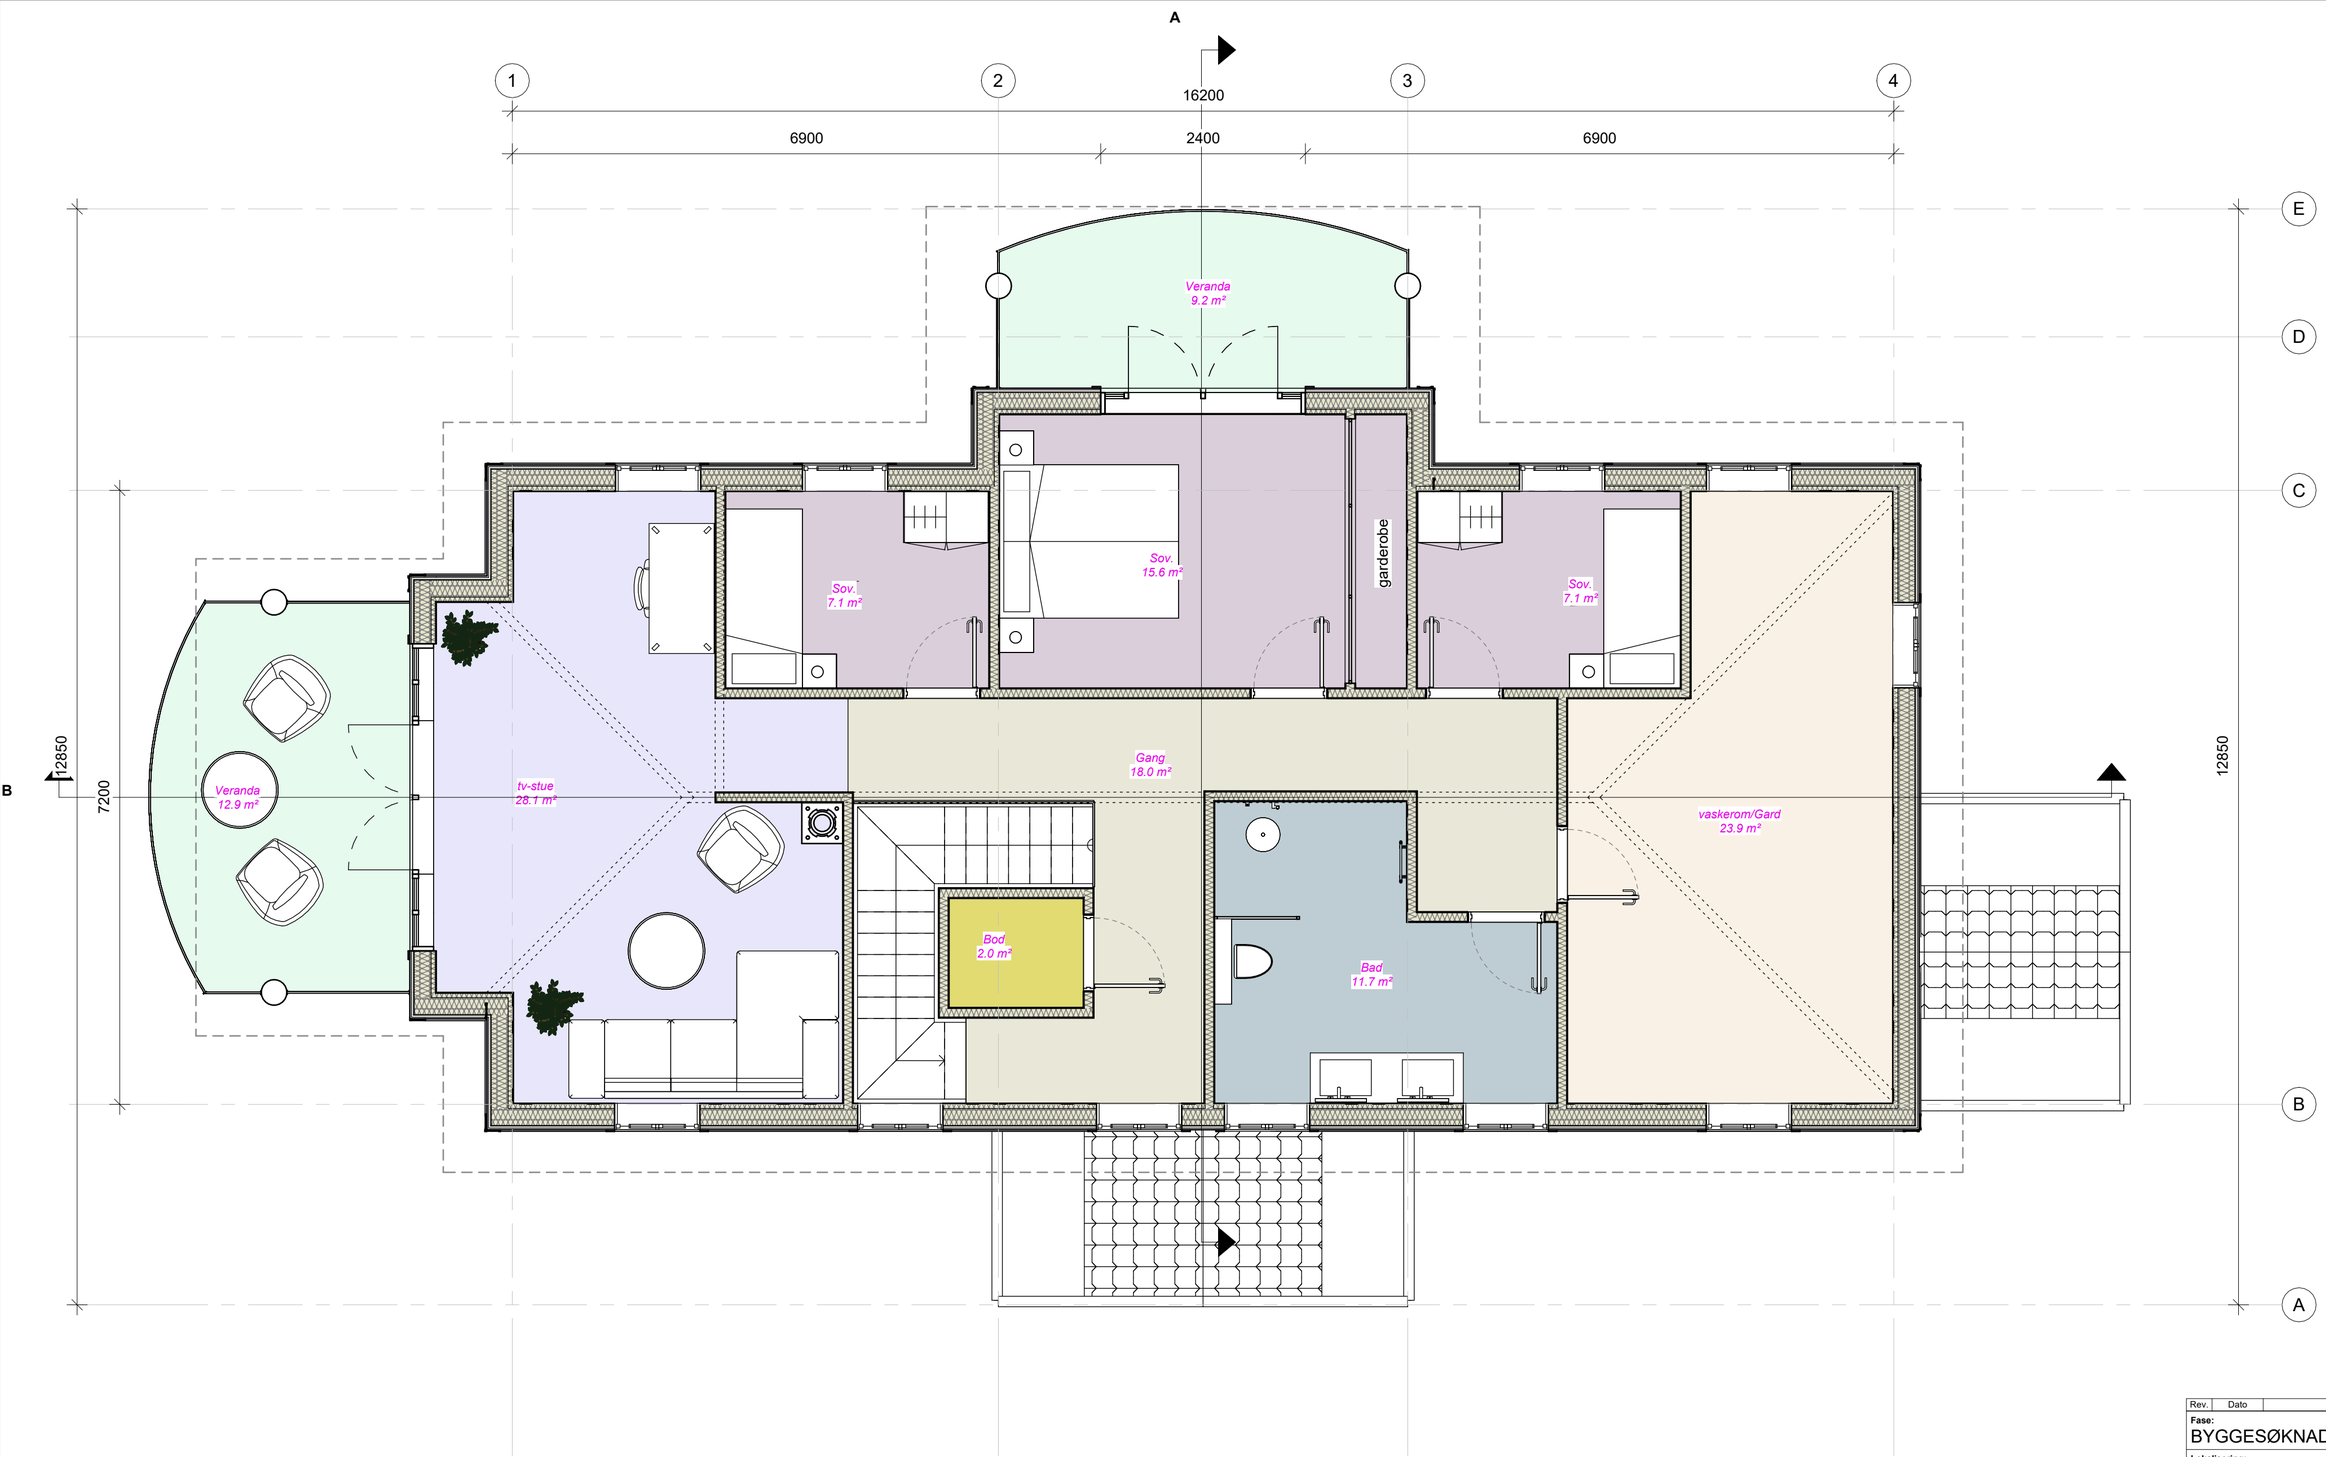

Rev.	Dato	Beskrivelse	Sign	Kontr

Fase:
BYGGESØKNAD

Lokalisering:
Bergen kommune
Nygårdsvikveien 38

Tittel:
Enebolig Silje Faugstad

Nygårdsvikveien 38

Tegn.: SAN
Dato: 26.11.25
Rev.
Format: A2
Målestokk: 1 : 50
Kontroll prosjekt
Sign.: RE
Kontroll: RE

Prosjektnr.: 1258
Tegningsnr.: A-30 03
Type tegning: Plan 03

ARKITEKT ROLV EIDE AS
Tel: 56332380
Postboks 325 5343 Straume
E-post: post@arkrolveide.no
www.arkrolveide.no