3 Ø

1 : 100

4 S

1 : 100

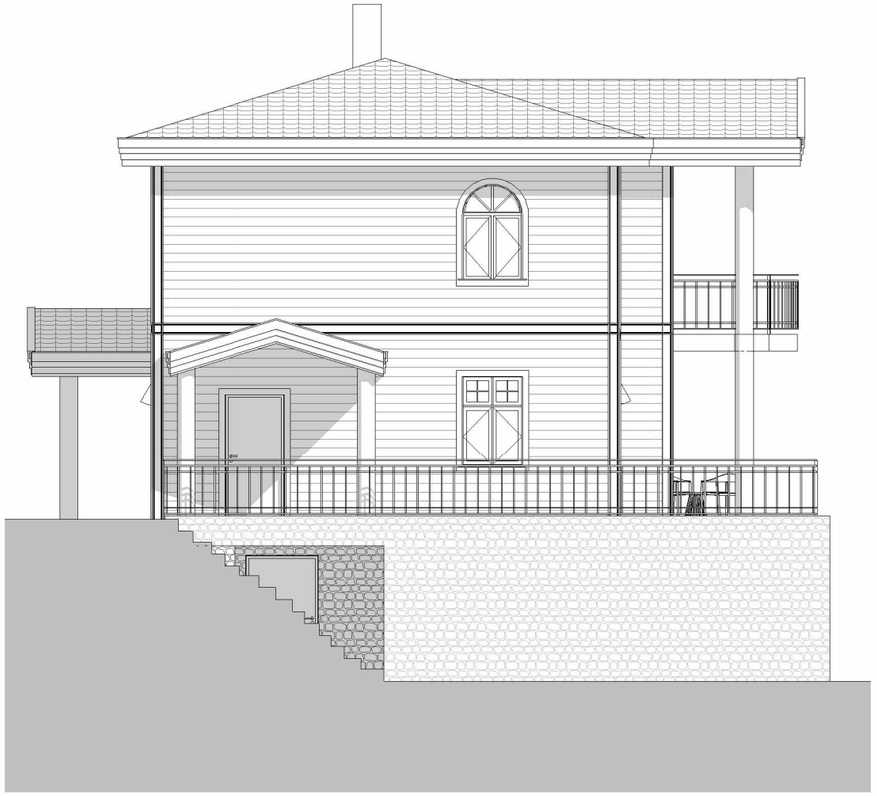

Tegningsnr.:	Revisjon nr.:
A-50 01	

Type tegning:
Fasader Sør og øst

Prosjekteringsgruppe:

ARK :

RIB :

RIV :

RIE :

RIBr :

RIAku :

Rev.	Dato	Beskrivelse	Sign	Kontr

Fase:
BYGGESØKNAD

Lokalisering:
Bergen kommune
Nygårdsvikveien 38

Tittel:
Enebolig Silje Faugstad

Nygårdsvikveien 38

Tegn.: SAN
Rev.
Dato: 26.11.25
Format: A3
Målestokk: 1 : 100
Kontroll prosjekt
Sign.: RE
Kontroll: RE

Prosjektnr.: 1258
Tegningsnr.: A-50 01

Type tegning:
Fasader Sør og øst

ARKITEKT ROLV EIDE AS
Tel: 56332380
Postboks 325 5343 Straume
E-post: post@arkrolveide.no
www.arkrolveide.no