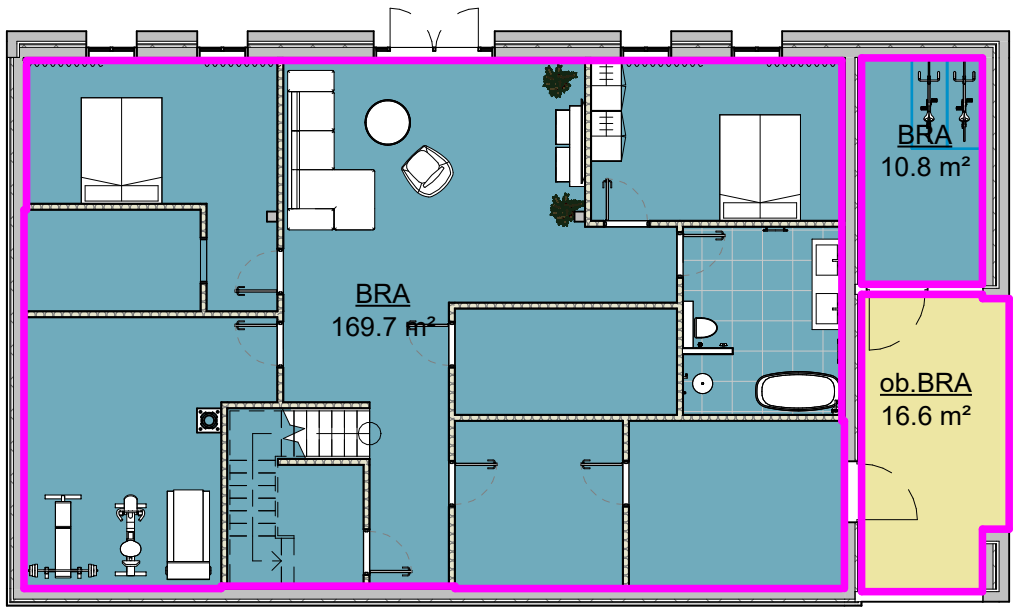

1 Plan 01

1 : 150

Areal (BRA)		
Level	Navn	Areal (m2)
Plan 01	BRA	169.7
Plan 01	BRA	10.8
		180.5
Plan 02	BRA	124.5
		124.5
Plan 03	BRA	124.5
		124.5
		429.5
Plan garasje	BRA GARASJE	38.8
		38.8
		38.8
Plan 01	ob.BRA	16.6
		16.6
Plan 02	ob.BRA	7.7
Plan 02	ob.BRA	6.7
Plan 02	ob.BRA	10.1
Plan 02	ob.BRA	6.9
		31.3
Plan 03	ob.BRA	6.9
Plan 03	ob.BRA	8.5
		15.4
		63.3
Grand total: 12		531.5

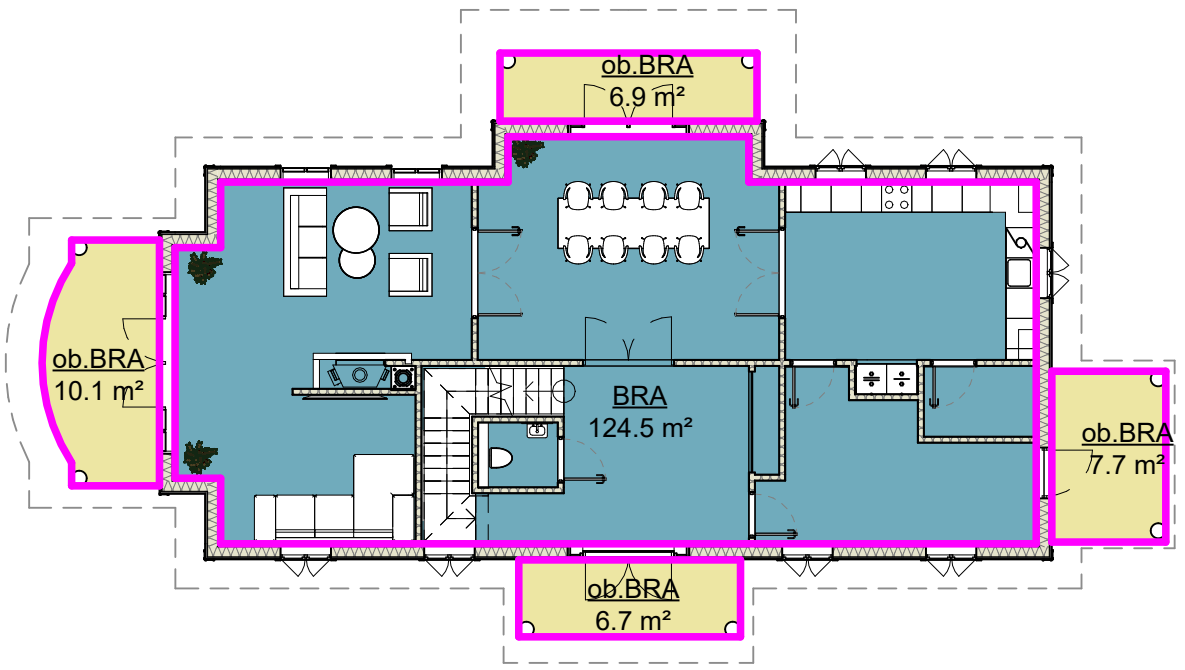

2 Plan 02

1 : 150

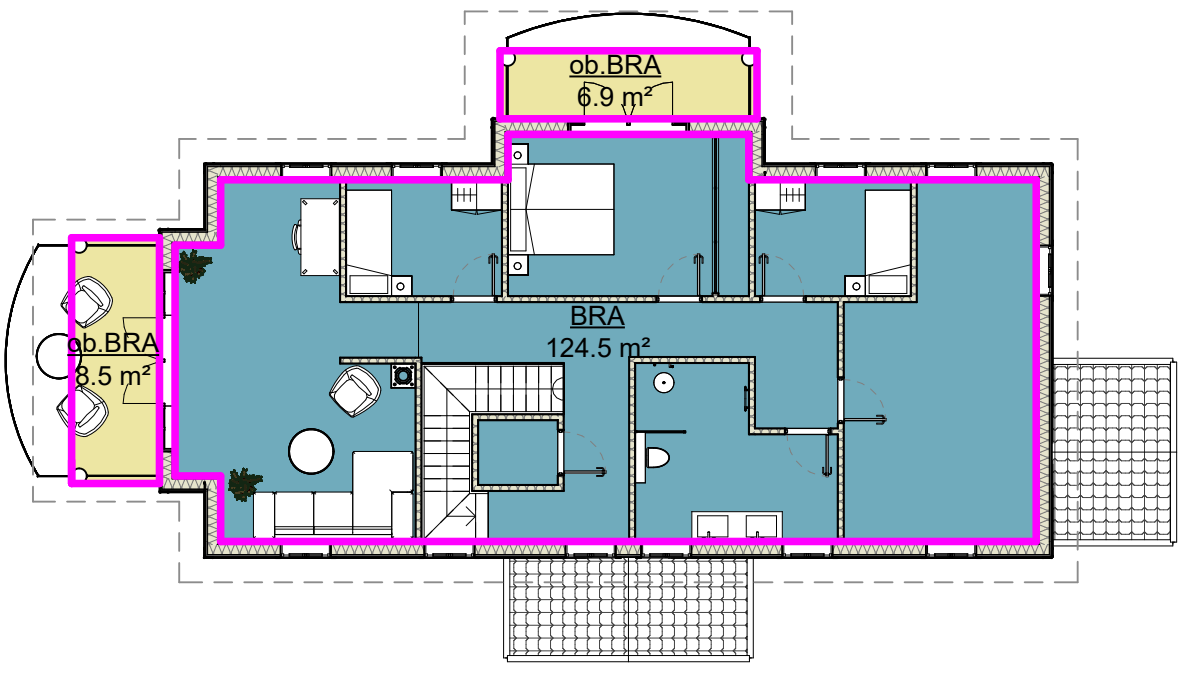

3 Plan 03

1 : 150

Rev.	Dato	Beskrivelse	Sign	Kontr

Fase: BYGGESØKNAD

Lokalisering:

Tittel:

Enebolig Silje Faugstad

Nygårdsvikveien 38

Bergen kommune
Nygårdsvikveien 38

Tegn.: SAN

Rev.

Dato: 26.11.25

Format: A3

Målestokk: 1 : 150

Kontroll prosjekt

Sign.: RE

Kontroll: RE

Prosjektnr.: 1258

Tegningsnr.: A-30 20

Type tegning: BRA

ARKITEKT ROLV EIDE AS
Tel: 56332380
Postboks 325 5343 Straume
E-post: post@arkrolveide.no
www.arkrolveide.no