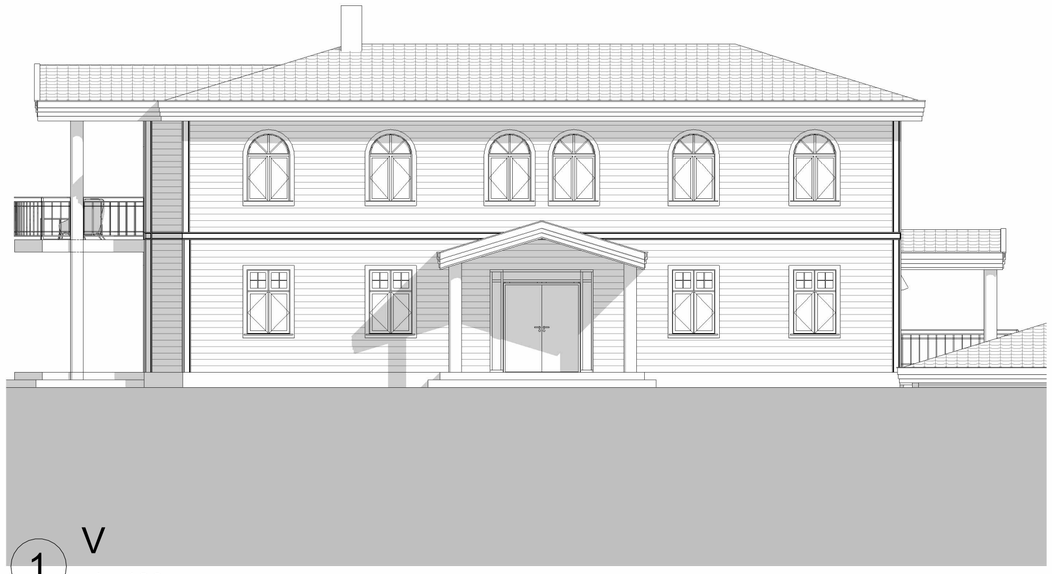

1 V
1 : 100

2 N
1 : 100

3 Ø
1 : 100

4 S
1 : 100

Tegningsnr.:	Revisjon nr.:
A-50 01	

Type tegning:
Fasader

Prosjekteringsgruppe:
ARK :
RIB :
RIV :
RIE :
RIBr :
RIAku :

Rev.	Dato	Beskrivelse	Sign	Kontr

Fase:
BYGGESØKNAD

Lokalisering:
Bergen kommune
Nygårdsvikveien 38

Tittel:
Enebolig Silje Faugstad

Nygårdsvikveien 38

Tegn.: SAN
Rev.
Dato: 26.11.25
Format: A2
Målestokk: 1 : 100
Kontroll prosjekt
Sign.: RE
Kontroll: RE

Prosjektnr.: 1258
Tegningsnr.: A-50 01
Type tegning: Fasader

ARKITEKT ROLV EIDE AS
Tel: 56332380
Postboks 325 5343 Straume
E-post: post@arkrolveide.no
www.arkrolveide.no